

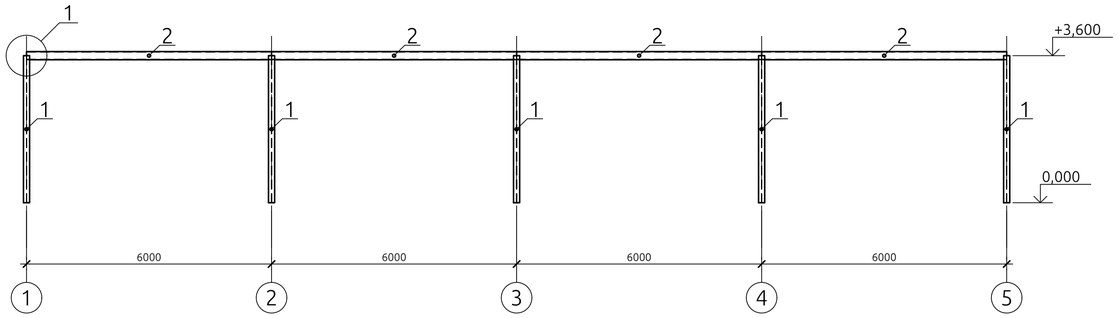



Фасад 1-5

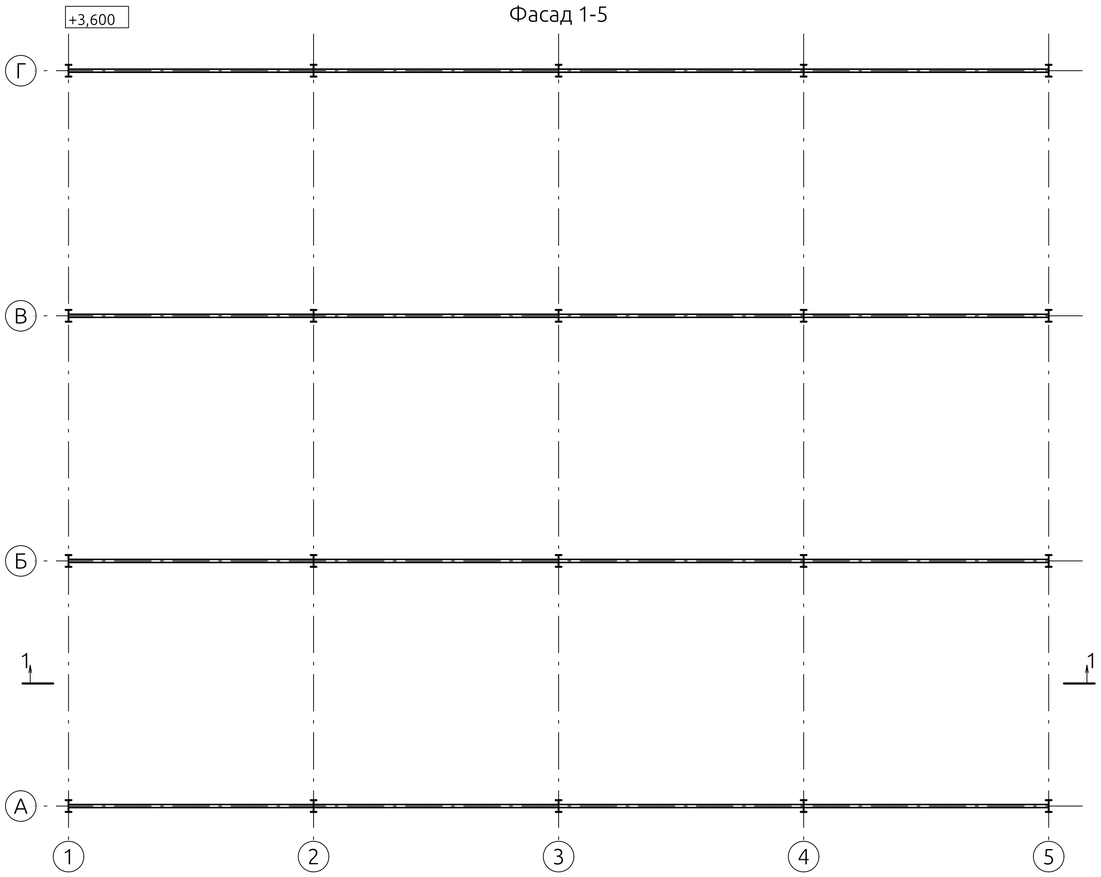

План на отм. +3,600

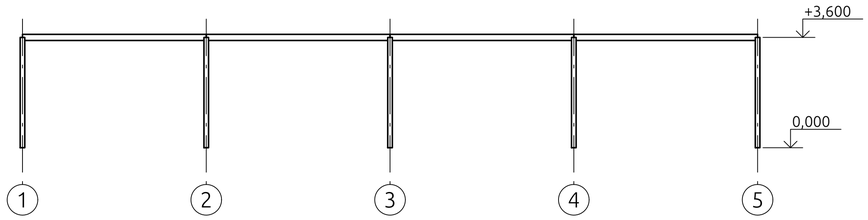

Разрез 1-1

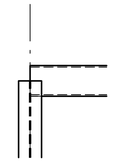

Узел 1

Спецификация металлопроката

Наименование профиля, ГОСТ, ТУ	Наименование или марка металла	Номер или размеры профиля, мм	№ п.п.	Масса металла по элементам конструкций, т		Общая масса, т
				Колонны	Балки	
Двутавры	S355	I 300×150×8×12	1	3,283		3,283
		Итого	2	3,283		3,283
Швеллеры	S235	С 200×75×6×10	3		1,944	1,944
		Итого	4		1,944	1,944
Всего масса металла			5	3,283	1,944	5,227
В том числе по маркам:						
	S235		6		1,944	1,944
	S355		7	3,283		3,283

Изм.	Кол.уч	Лист	№ док.	Подп.	Дата	0000-КМ		
Разраб.								
Пров.								
Н. контр.						Схема расположения элементов - Контрольное здание	Стадия	Лист	Листов
							Р		1

Взам. инв. №

Подп. и дата

Инв. № подл.

Формат А1