Ведомость рабочих чертежей основного комплекта

Лист	Наименование	Примечание
1	Общие данные	Изм. 1; 2 (Зам.)
2	Колонна К1	
3	Балка	Изм. 1; 2

Ведомость ссылочных и прилагаемых документов

Обозначение	Наименование	Примечание
	Ссылочные документы	
2345-26-КМ	Конструкции металлические. Рабочие чертежи	
ГОСТ 5264-80	Ручная дуговая сварка. Соединения сварные. Основные типы, конструктивные элементы и размеры	

Общие указания

1. Масса металлоконструкций по модели — 5,267 т, марки стали: S235, S355.

2. Сварные соединения — по ГОСТ 5264-80, катеты швов — по чертежам.

3. Сварочные материалы — по таблице Г.1 СП 16.13330.2017 для марок стали свариваемых деталей.

4. Размеры — в миллиметрах.

Взам. инв. №

Подп. и дата

Инв. № подл. 1234

Изм.	Кол.уч	Лист	№ док.	Подп.	Дата
2	-	Зам.	16-26		22.10.26
1	-	Зам.	15-26		21.10.26
Разраб.		Иванов			19.10.26
Пров.		Смирнов			19.10.26
Н. контр.		Петров			20.10.26
ГИП		Сидоров			20.10.26

2345-26-КМД

Производственный корпус


Каркас здания

Стадия	Лист	Листов
Р	1	3


Общие данные

ООО «Проект»

Формат А3

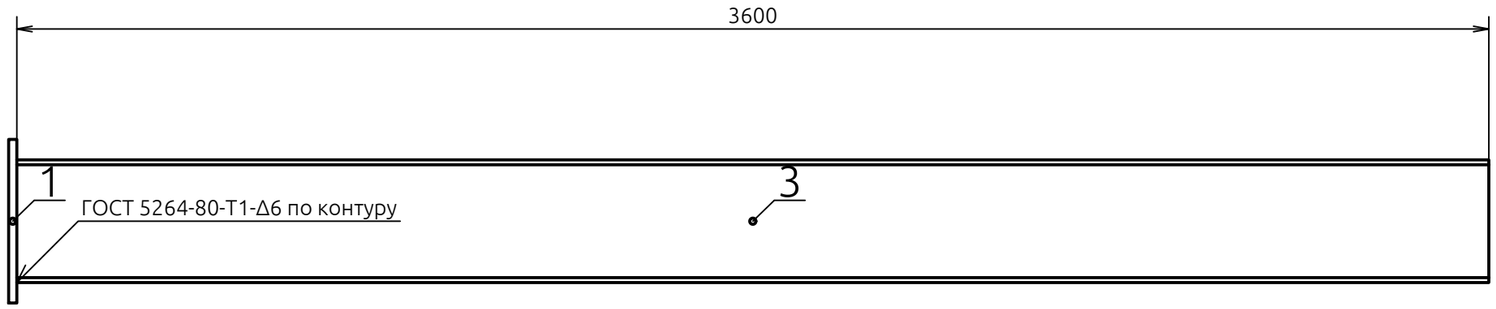

Вид спереди 1:15

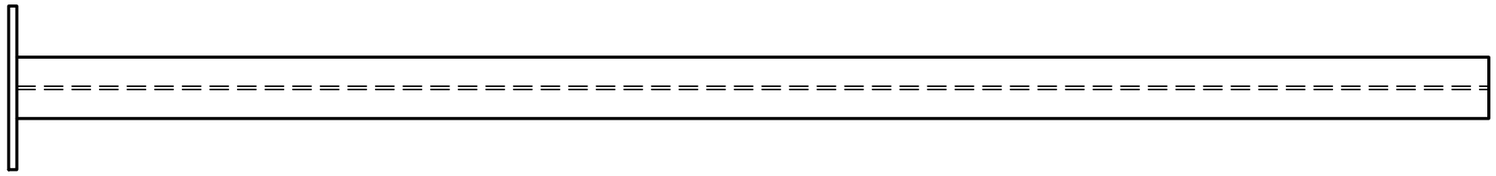

Вид сверху 1:15

Спецификация

Поз.	Обозначение	Наименование	Кол.	Масса ед., кг	Приме-чание
		Детали			
1		—20×400, L=400	1	25,120	S235
3		I 300×150×8×12, L=3600	1	164,134	S355

Изм.	Кол.уч	Лист	№ док.	Подп.	Дата
Разраб.		Иванов			19.10.26
Пров.		Смирнов			19.10.26
Н. контр.		Петров			20.10.26
ГИП		Сидоров			20.10.26


2345-26-КМД

Производственный корпус

Каркас здания	Стадия	Лист	Листов
	Р	2	
Колонна К1	ООО «Проект»		


Взам. инв. №	
Подп. и дата	
Инв. № подл.	1234

Формат А3

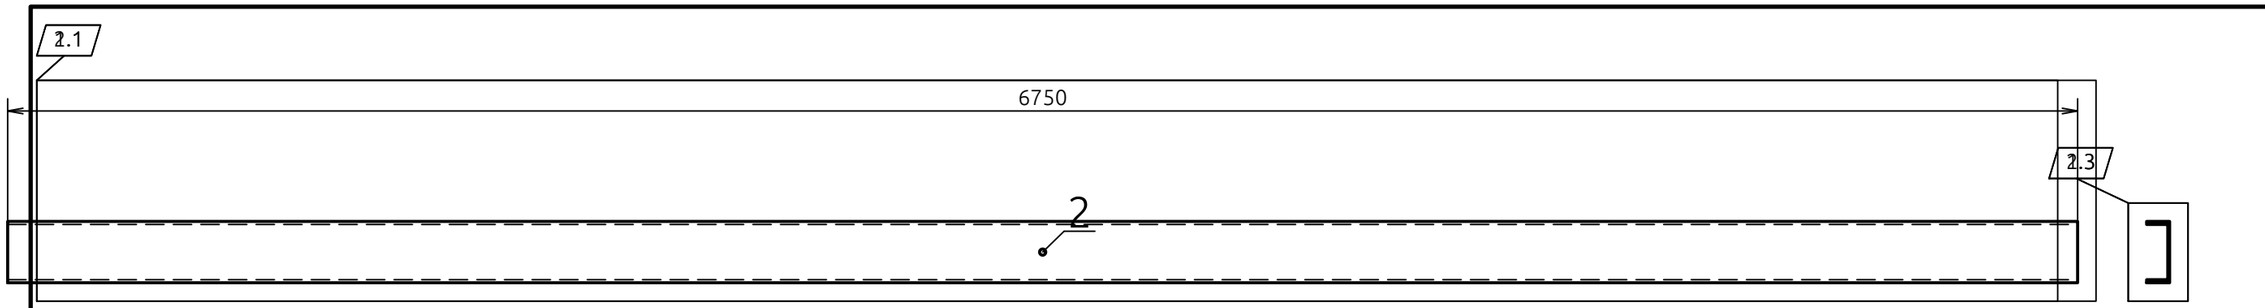

Вид спереди 1:20

Вид слева 1:20

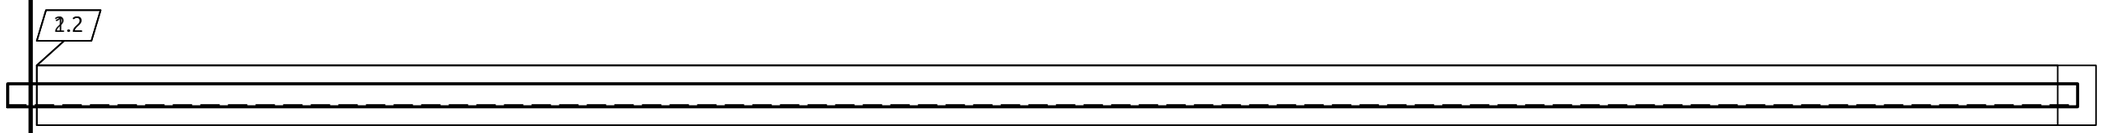

Вид сверху 1:20

Взам. инв. №	
Подп. и дата	
Инв. № подл.	1234

Изм.	Кол.уч	Лист	№ док.	Подп.	Дата
2	3	-	16-26		22.10.26
1	3	-	15-26		21.10.26
Разраб.		Иванов			19.10.26
Пров.		Смирнов			19.10.26
Н. контр.		Петров			20.10.26
ГИП		Сидоров			20.10.26

2345-26-КМД

Производственный корпус

Каркас здания	Стадия	Лист	Листов
	Р	3	
Балка	ООО «Проект»		

Формат А3