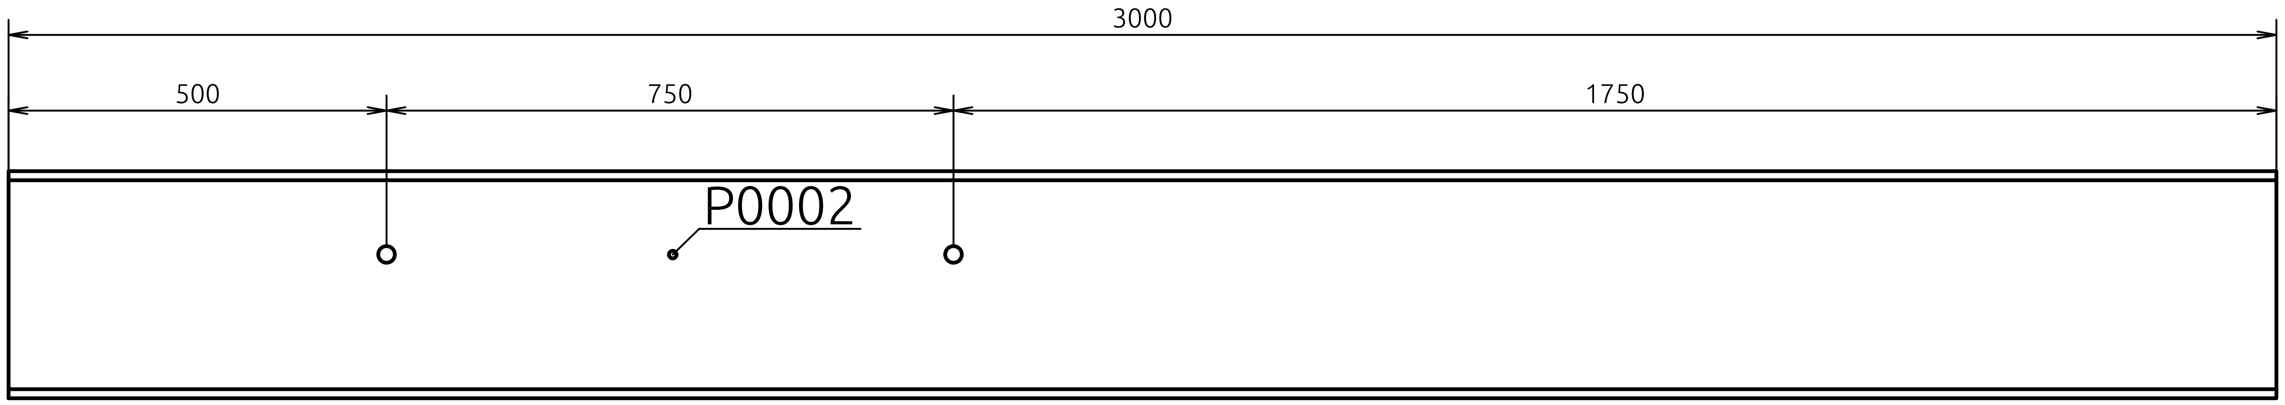

Вид спереди 1:10

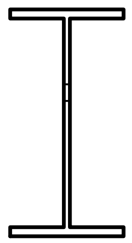

Вид слева 1:10

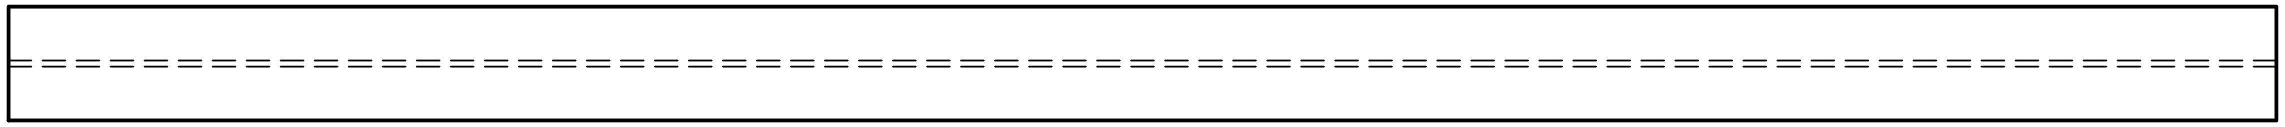

Вид сверху 1:10

Взам. инв. №

Подп. и дата

Инв. № подл.

Изм.	Кол.уч	Лист	№ док.	Подп.	Дата
Разраб.					
Пров.					
Н. контр.					

0000-КМД

Стадия	Лист	Листов
Р		1

Балка Б1

Формат А3

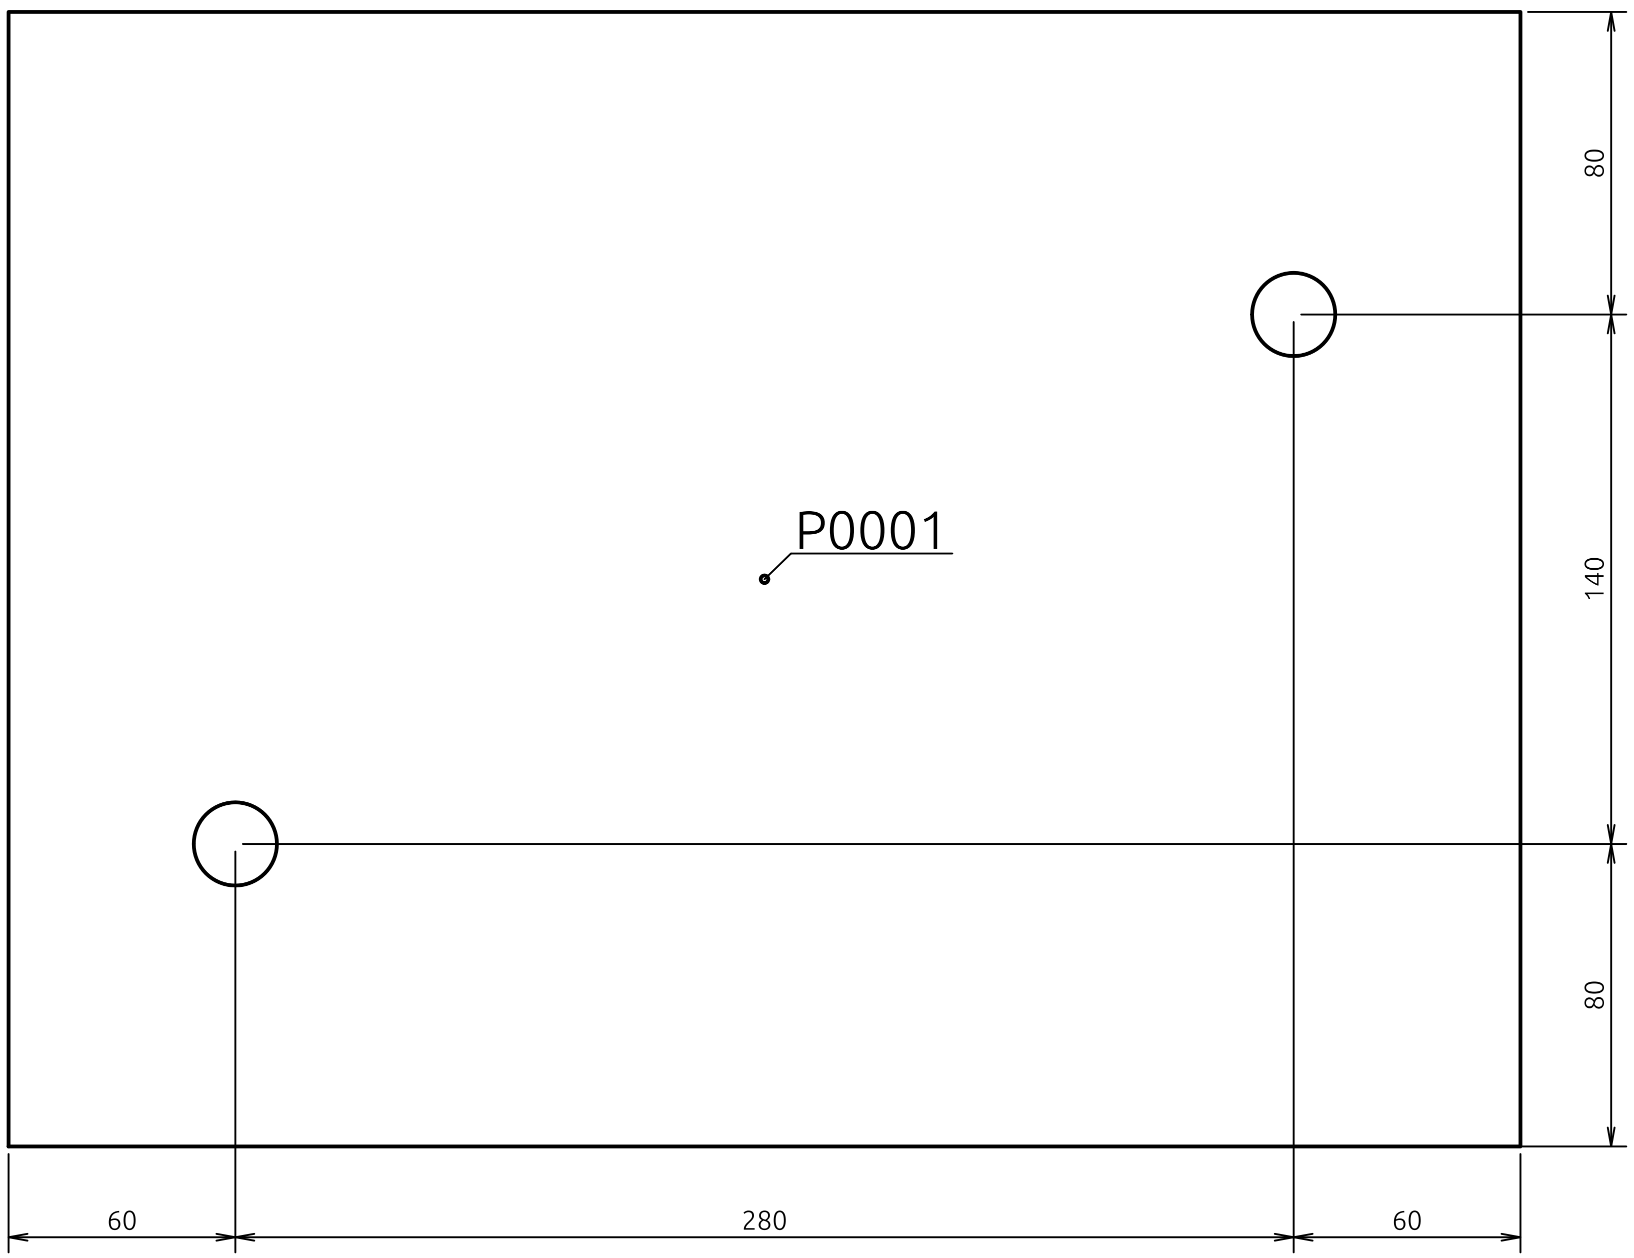

Вид на плиту 1:2

Взам. инв. №

Подп. и дата

Инв. № подл.

Изм.	Кол.уч	Лист	№ док.	Подп.	Дата
Разраб.					
Пров.					
Н. контр.					

0000-КМД			
	Стадия	Лист	Листов
	Р		1
Пластина П1			

Формат А3

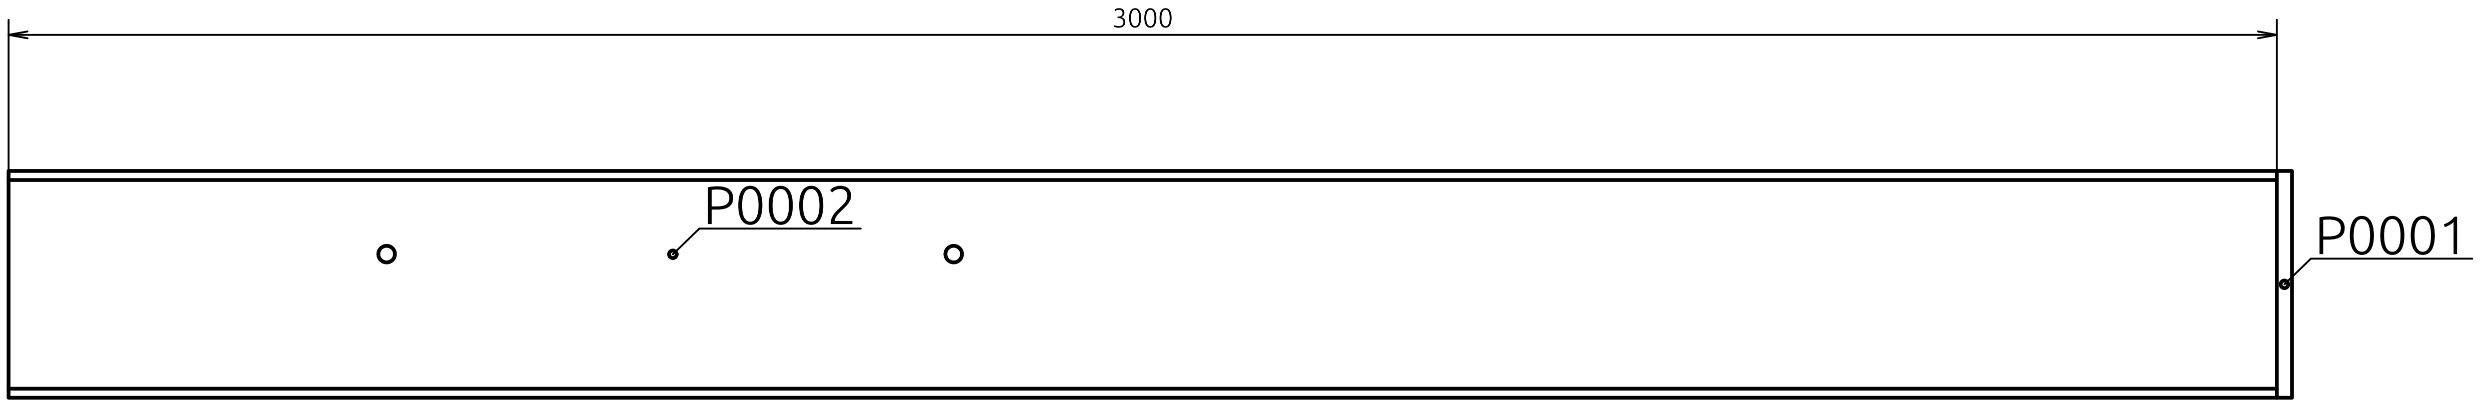

Вид спереди 1:10

 

Вид сверху 1:10

Спецификация

Поз.	Обозначение	Наименование	Кол.	Масса ед., кг	Приме-чание
		Детали			
P0001		—20×300, L=400	1	18,721	S235
P0002		I 300×150×8×12, L=3000	1	136,731	S235

Изм.	Кол.уч	Лист	№ док.	Подп.	Дата	0000-КМД		
Разраб.								
Пров.								
							Стадия	Лист	Листов
							Р		1
Н. контр.						Балка в сборе Б1		

Взам. инв. №

Подп. и дата

Инв. № подл.

Формат А3

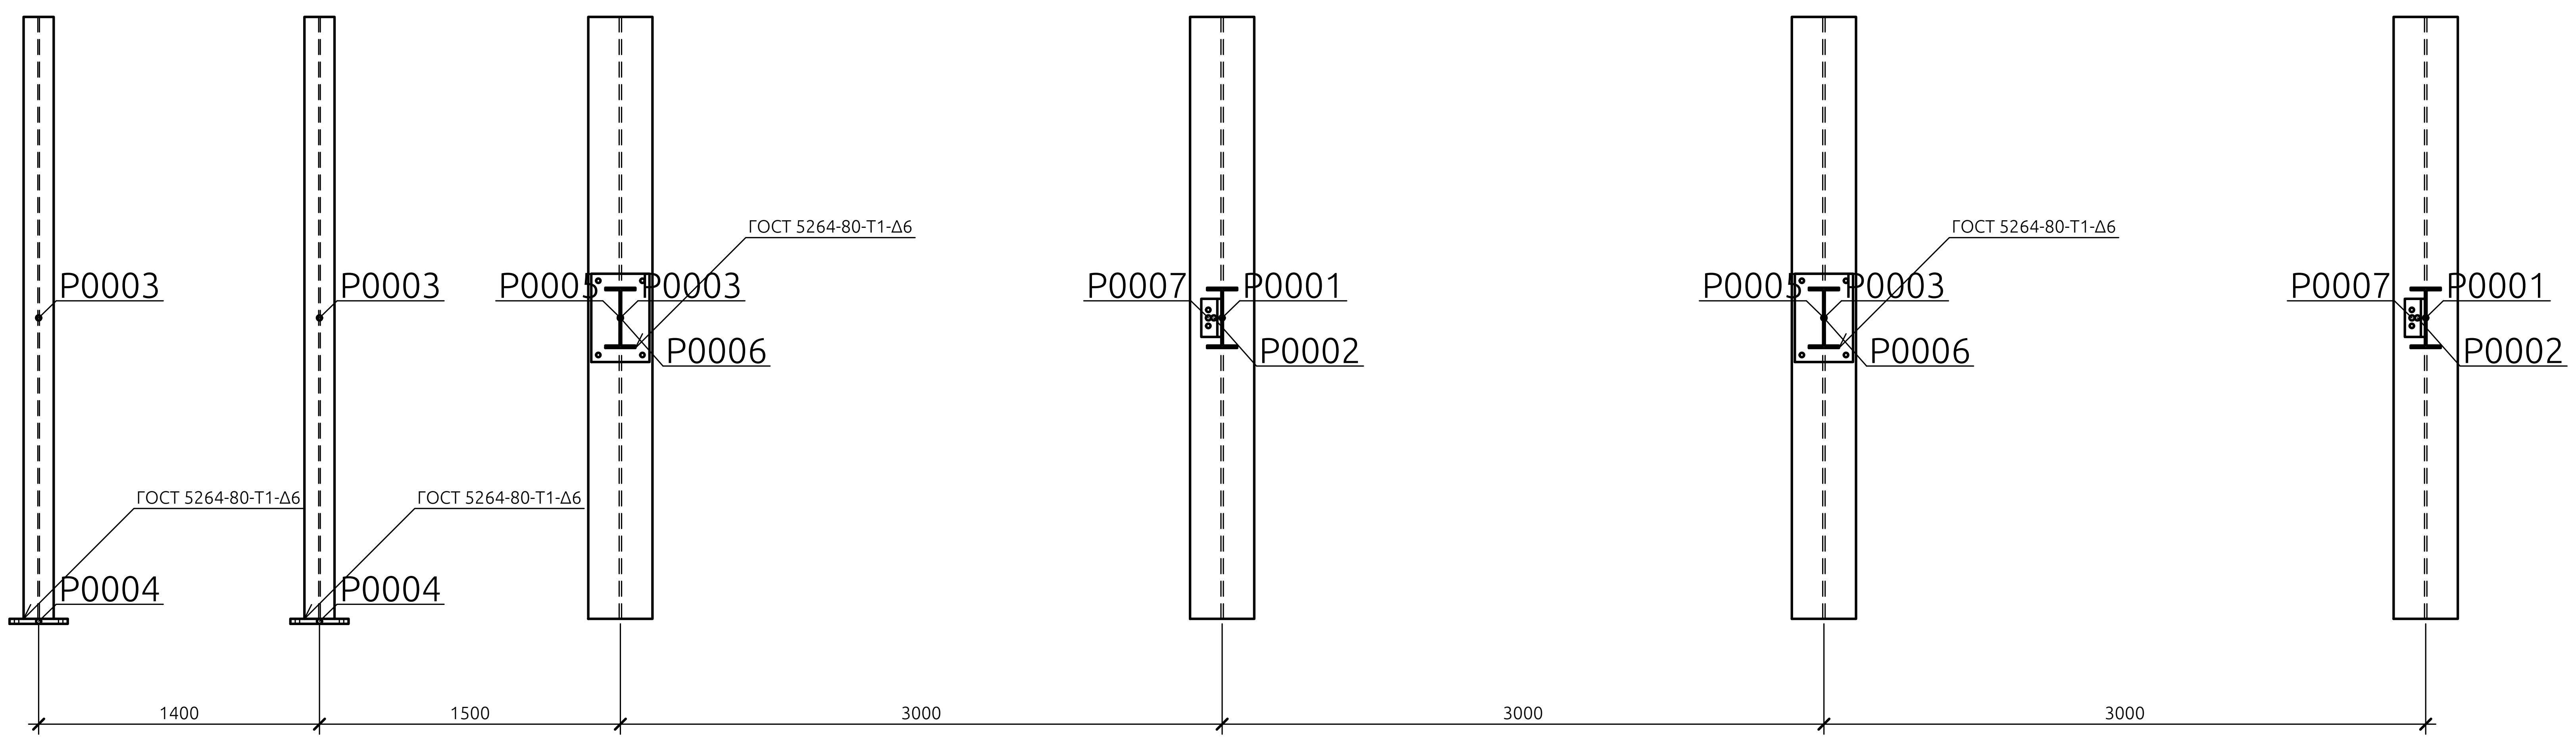

Фасад по оси А

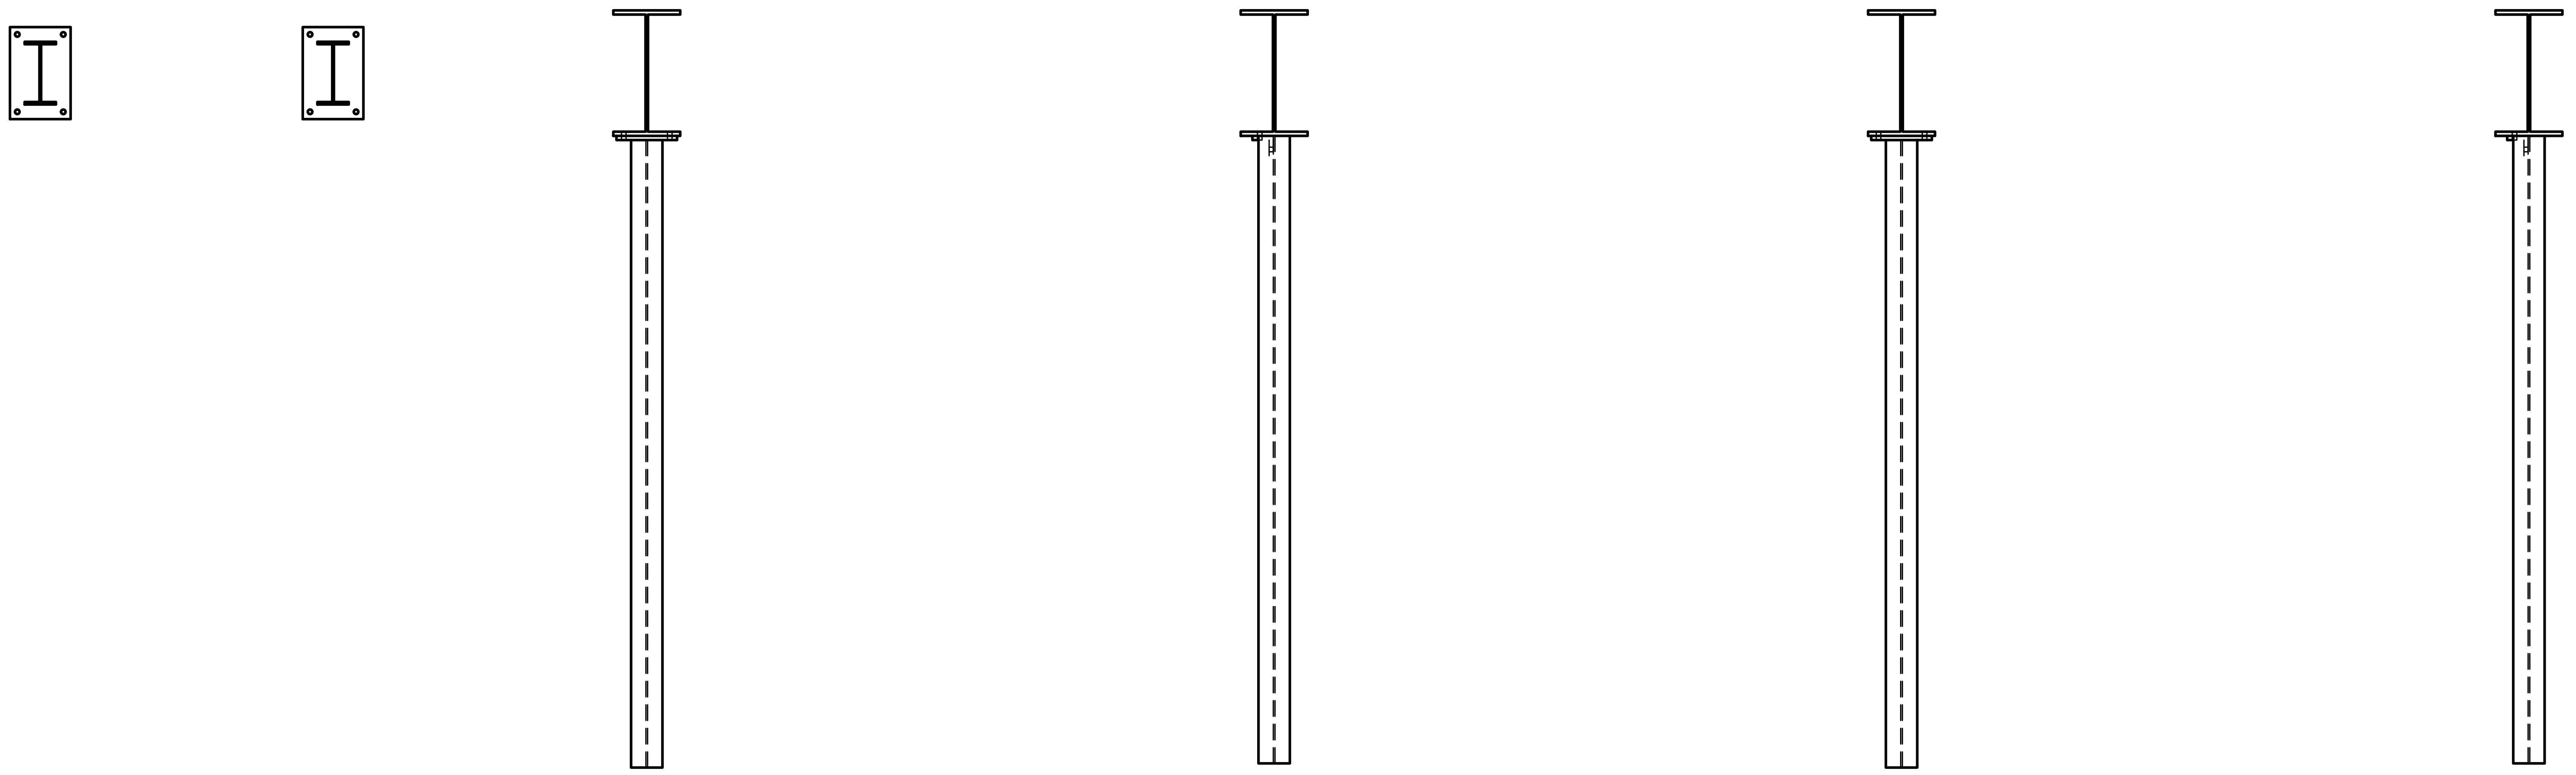

План

Спецификация металлопроката

Наименование профиля, ГОСТ, ТУ	Наименование или марка металла	Номер или размеры профиля, мм	№ п.п.	Масса металла по элементам конструкций, т			Общая масса, т
				Колонны	Балки	Прочие	
Двутавры	S235	I 300×150×8×12	1	0,274	0,547		0,821
	S235	I600 GUI support	2	1,838			1,838
		Итого	3	2,112	0,547		2,659
Прокат листовой	S235	—20	4			0,040	0,040
	S235	—25	5			0,049	0,049
		Итого	6			0,089	0,089
Уголки	S235	L 100×100×20	7		0,010		0,010
		Итого	8		0,010		0,010
Всего масса металла			9	2,112	0,557	0,089	2,758
В том числе по маркам:							
	S235		10	2,112	0,557	0,089	2,758

Взам. инв. №

Подп. и дата

Инв. № подл.

Изм.	Кол.уч	Лист	№ док.	Подп.	Дата
Разраб.					
Пров.					
Н. контр.					

0000-КМ

Стадия	Лист	Листов
Р		1

Схема расположения элементов · Connection GUI fixture

Формат А1