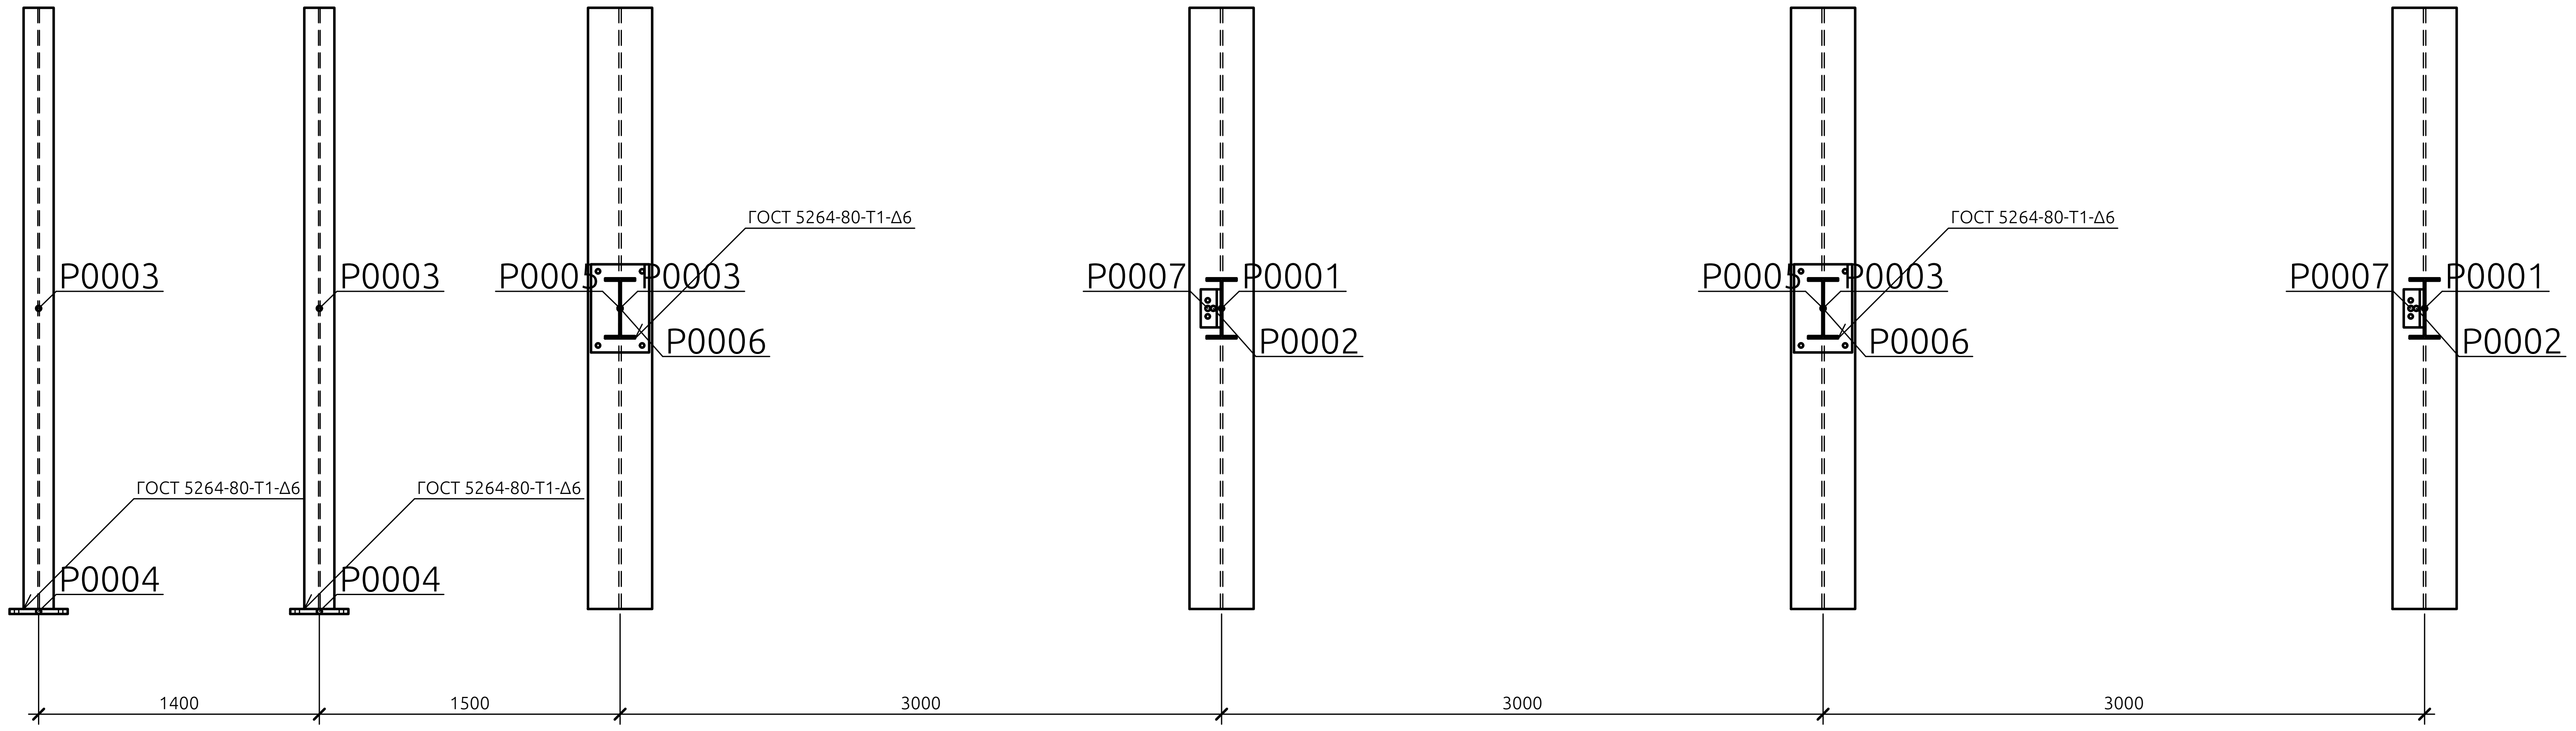

Фасад по оси А

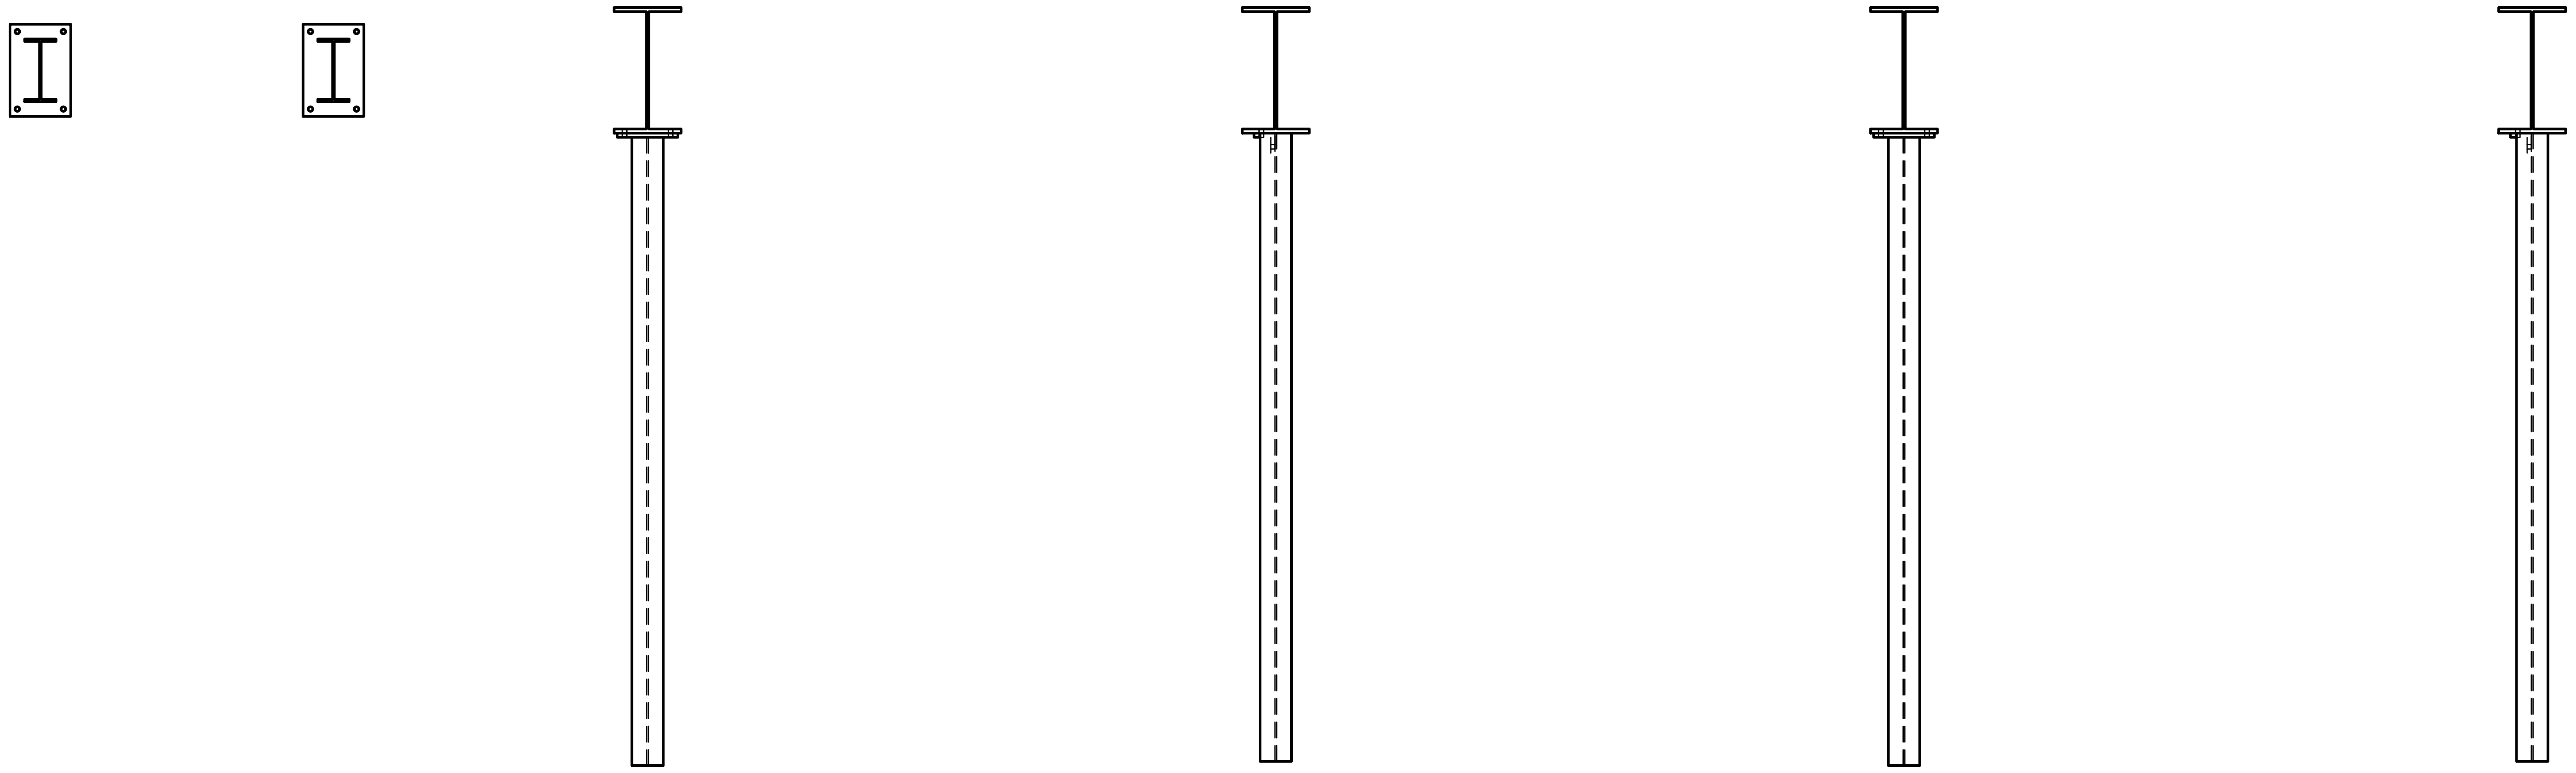

План

## Спецификация металлопроката

| Наименование профиля, ГОСТ, ТУ | Наименование или марка металла | Номер или размеры профиля, мм | № п.п. | Масса металла по элементам конструкций, т | | | Общая масса, т |
|---|---|---|---|---|---|---|---|
| | | | | Колонны | Балки | Прочие | |
| Двутавры | S235 | I 300×150×8×12 | 1 | 0,274 | 0,547 | | 0,821 |
| | S235 | I600 GUI support | 2 | 1,838 | | | 1,838 |
| | | Итого | 3 | 2,112 | 0,547 | | 2,659 |
| Прокат листовой | S235 | —20 | 4 | | | 0,040 | 0,040 |
| | S235 | —25 | 5 | | | 0,049 | 0,049 |
| | | Итого | 6 | | | 0,089 | 0,089 |
| Уголки | S235 | L 100×100×20 | 7 | | 0,010 | | 0,010 |
| | | Итого | 8 | | 0,010 | | 0,010 |
| Всего масса металла | | | 9 | 2,112 | 0,557 | 0,089 | 2,758 |
| В том числе по маркам: | | | | | | | |
| | S235 | | 10 | 2,112 | 0,557 | 0,089 | 2,758 |

| Изм. | Кол.уч | Лист | № док. | Подп. | Дата | 0000-КМ | | |
|---|---|---|---|---|---|---|---|---|
| Разраб. | | | | | | | | |
| Пров. | | | | | | | Стадия | Лист | Листов |
| | | | | | | | Р | | 1 |
| Н. контр. | | | | | | Схема расположения элементов · Connection GUI fixture | | |

Формат А1

Взам. инв. №

Подп. и дата

Инв. № подл.