## Ведомость рабочих чертежей основного комплекта

| Лист | Наименование | Примечание |
|---|---|---|
| 1 | Общие данные | Изм. 1 (Зам.) |
| 2 | Схема расположения элементов · Контрольное здание | Изм. 1 |

## Ведомость ссылочных и прилагаемых документов

| Обозначение | Наименование | Примечание |
|---|---|---|
| | Ссылочные документы | |
| ГОСТ 5264-80 | Ручная дуговая сварка. Соединения сварные. Основные типы, конструктивные элементы и размеры | |

## Ведомость основных комплектов рабочих чертежей

| Обозначение | Наименование | Примечание |
|---|---|---|
| 2345-26-КМ | Конструкции металлические | |
| 2345-26-КМД | Конструкции металлические деталировочные | |

## Общие указания

1. Масса металлоконструкций по модели — 5,262 т, марки стали: S235, S355.

2. Сварные соединения — по ГОСТ 5264-80, катеты швов — по чертежам.

3. Размеры — в миллиметрах, отметки — в метрах.

| Взам. инв. № | |
|---|---|
| Подп. и дата | |
| Инв. № подл. | 1234 |


| | | | | | |
|---|---|---|---|---|---|
| 1 | - | Зам. | 15-26 | | 20.10.26 |
| Изм. | Кол.уч | Лист | № док. | Подп. | Дата |
| Разраб. | | Иванов | | | 19.10.26 |
| Пров. | | Смирнов | | | 19.10.26 |
| Н. контр. | | Петров | | | 20.10.26 |
| ГИП | | Сидоров | | | 20.10.26 |

2345-26-КМ


Производственный корпус

| Каркас здания | Стадия | Лист | Листов |
|---|---|---|---|
| | Р | 1 | 2 |
| Общие данные | ООО «Проект» | | |

Формат А3

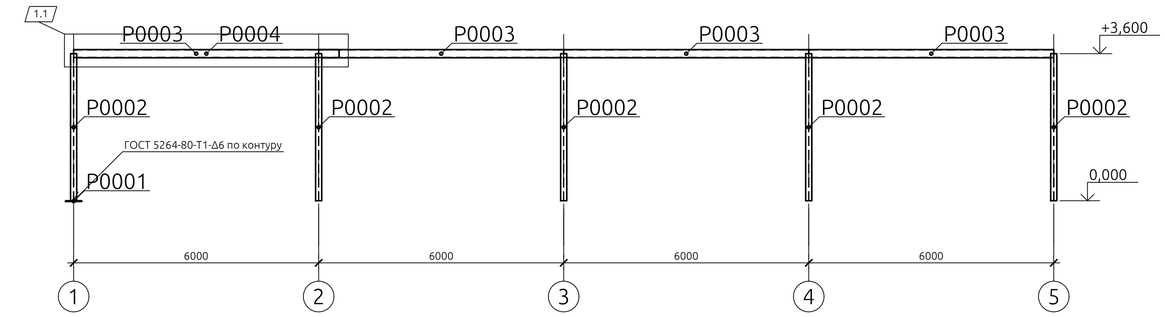


Фасад 1-5

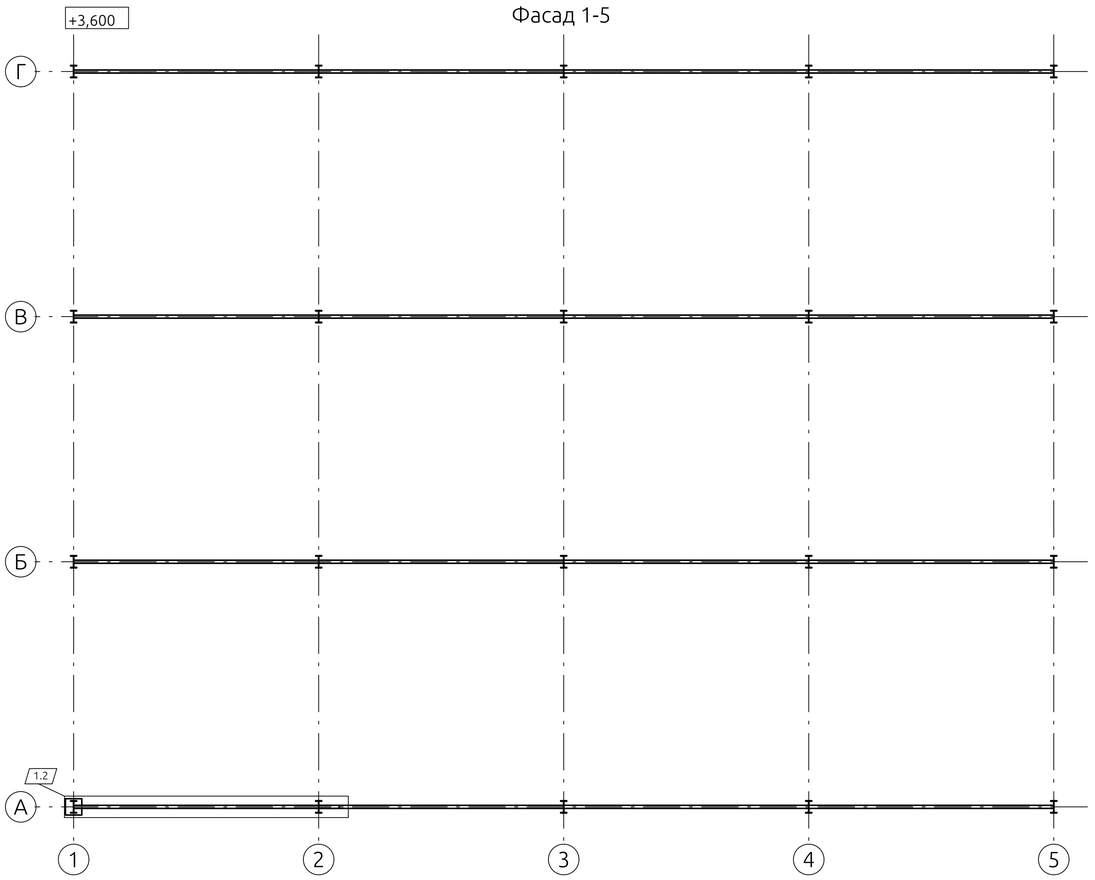


План на отм. +3,600

1.3

## Спецификация металлопроката

| Наименование профиля, ГОСТ, ТУ | Наименование или марка металла | Номер или размеры профиля, мм | № п.п. | Масса металла по элементам конструкций, т | | Общая масса, т |
|---|---|---|---|---|---|---|
| | | | | Колонны | Балки | |
| Двутавры | S355 | I 300×150×8×12 | 1 | 3,283 | | 3,283 |
| | | Итого | 2 | 3,283 | | 3,283 |
| Прокат листовой | S235 | —20 | 3 | 0,025 | | 0,025 |
| | | Итого | 4 | 0,025 | | 0,025 |
| Швеллеры | S235 | С 200×75×6×10 | 5 | | 1,954 | 1,954 |
| | | Итого | 6 | | 1,954 | 1,954 |
| Всего масса металла | | | 7 | 3,308 | 1,954 | 5,262 |
| В том числе по маркам: | | | | | | |
| | S235 | | 8 | 0,025 | 1,954 | 1,980 |
| | S355 | | 9 | 3,283 | | 3,283 |

| Изм. | Кол.уч | Лист | № док. | Подп. | Дата |
|---|---|---|---|---|---|
| 1 | 3 | - | 15-26 | | 20.10.26 |
| Разраб. | | Иванов | | | 19.10.26 |
| Пров. | | Смирнов | | | 19.10.26 |
| Н. контр. | | Петров | | | 20.10.26 |
| ГИП | | Сидоров | | | 20.10.26 |

2345-26-КМ

Производственный корпус

Каркас здания

| Стадия | Лист | Листов |
|---|---|---|
| Р | 2 | |

Схема расположения элементов · Контрольное здание

ООО «Проект»

Взам. инв. №

Подп. и дата

Инв. № подл. 1234

Формат А1