Ведомость рабочих чертежей основного комплекта

Лист	Наименование	Примечание
1	Общие данные	Изм. 1; 2 (Зам.)
2	Схема расположения элементов · Контрольное здание	Изм. 1; 2

Ведомость ссылочных и прилагаемых документов

Обозначение	Наименование	Примечание
	Ссылочные документы	
ГОСТ 5264-80	Ручная дуговая сварка. Соединения сварные. Основные типы, конструктивные элементы и размеры	

Ведомость основных комплектов рабочих чертежей

Обозначение	Наименование	Примечание
2345-26-КМ	Конструкции металлические	
2345-26-КМД	Конструкции металлические деталировочные	

Общие указания

1. Масса металлоконструкций по модели — 5,267 т, марки стали: S235, S355.

2. Сварные соединения — по ГОСТ 5264-80, катеты швов — по чертежам.

3. Размеры — в миллиметрах, отметки — в метрах.

Взам. инв. №

Подп. и дата

Инв. № подл. 1234


Изм.	Кол.уч	Лист	№ док.	Подп.	Дата
2	-	Зам.	16-26		22.10.26
1	-	Зам.	15-26		21.10.26
Разраб.		Иванов			19.10.26
Пров.		Смирнов			19.10.26
Н. контр.		Петров			20.10.26
ГИП		Сидоров			20.10.26

2345-26-КМ


Производственный корпус

Каркас здания	Стадия	Лист	Листов
	Р	1	2
Общие данные	ООО «Проект»		

Формат А3

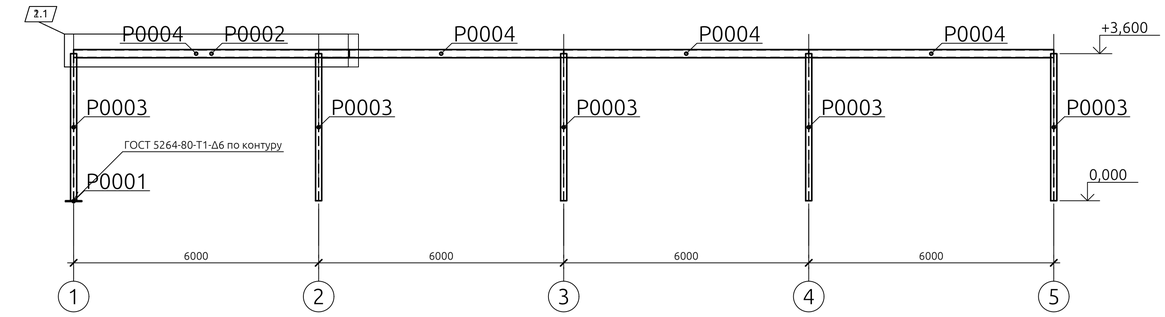

Фасад 1-5

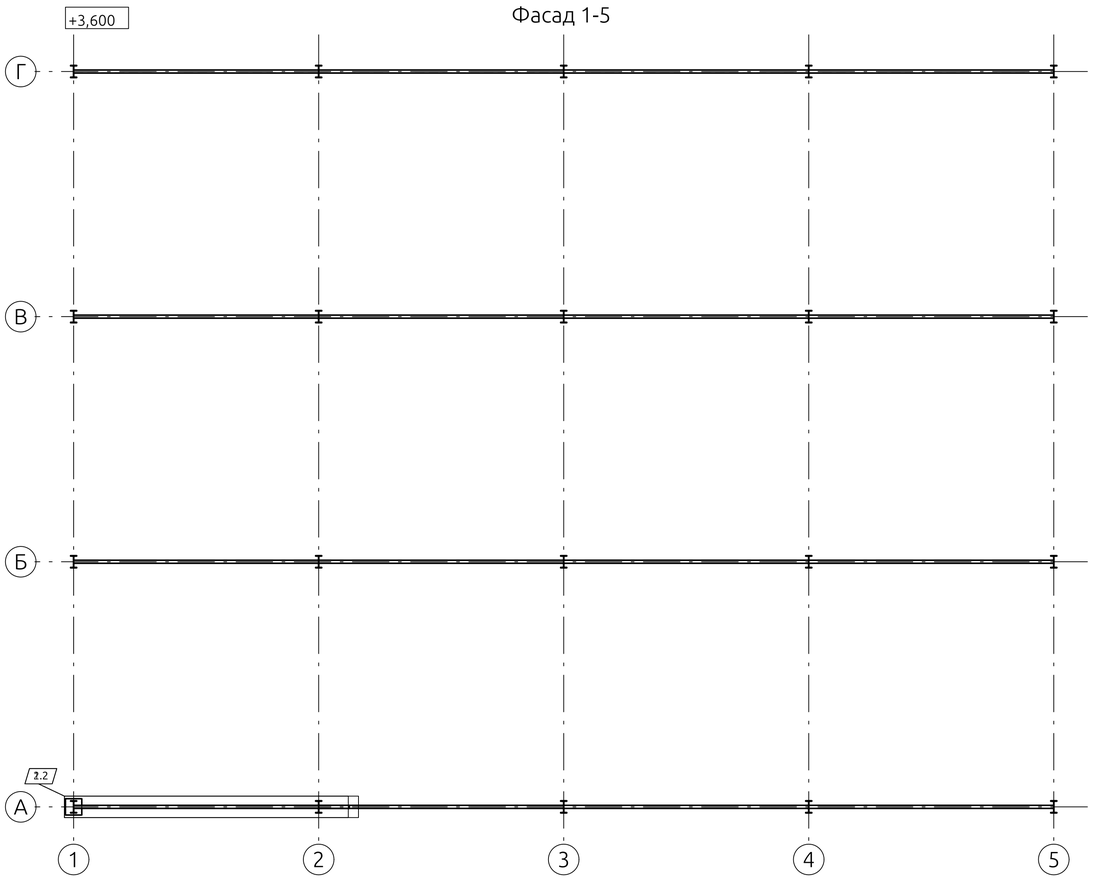

План на отм. +3,600

2.3

Спецификация металлопроката

Наименование профиля, ГОСТ, ТУ	Наименование или марка металла	Номер или размеры профиля, мм	№ п.п.	Масса металла по элементам конструкций, т		Общая масса, т
				Колонны	Балки	
Двутавры	S355	I 300×150×8×12	1	3,283		3,283
		Итого	2	3,283		3,283
Прокат листовой	S235	—20	3	0,025		0,025
		Итого	4	0,025		0,025
Швеллеры	S235	С 200×75×6×10	5		1,959	1,959
		Итого	6		1,959	1,959
Всего масса металла			7	3,308	1,959	5,267
В том числе по маркам:						
	S235		8	0,025	1,959	1,985
	S355		9	3,283		3,283

2	3	-	16-26		22.10.26
1	3	-	15-26		21.10.26
Изм.	Кол.уч	Лист	№ док.	Подп.	Дата
Разраб.		Иванов			19.10.26
Пров.		Смирнов			19.10.26
Н. контр.		Петров			20.10.26
ГИП		Сидоров			20.10.26

2345-26-КМ

Производственный корпус

Каркас здания	Стадия	Лист	Листов
	Р	2	

Схема расположения элементов · Контрольное здание

ООО «Проект»

Взам. инв. №

Подп. и дата

Инв. № подл. 1234

Формат А1