


Фасад 1-5

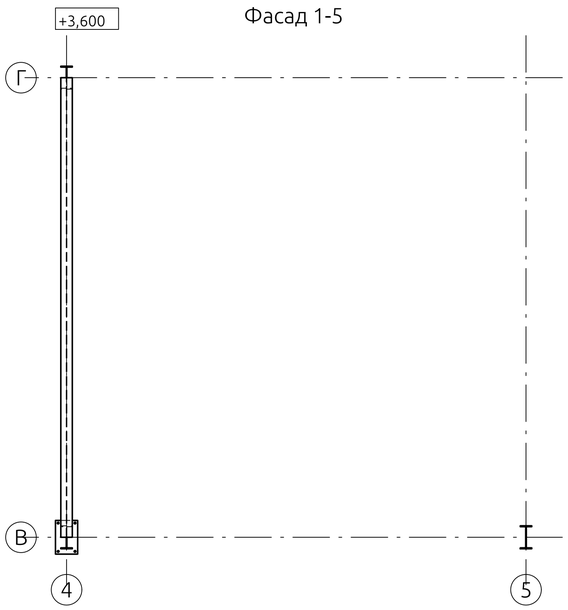

План на отм. +3,600

Спецификация металлопроката

Наименование профиля, ГОСТ, ТУ	Наименование или марка металла	Номер или размеры профиля, мм	№ п.п.	Масса металла по элементам конструкций, т			Общая масса, т
				Колонны	Балки	Прочие	
Двутавры	S235	I 300×150×8×12	1	0,492	0,274		0,766
		Итого	2	0,492	0,274		0,766
Прокат листовой	S235	—20	3			0,020	0,020
		Итого	4			0,020	0,020
Всего масса металла			5	0,492	0,274	0,020	0,786
В том числе по маркам:							
	S235		6	0,492	0,274	0,020	0,786


Изм.	Кол.уч	Лист	№ док.	Подп.	Дата	0000-КМ		
Разраб.								
Пров.								
Н. контр.						Схема расположения элементов · Новый проект	Стадия	Лист	Листов
							Р		1

Взам. инв.№

Подп. и дата

Инв. №подл.


Формат А1

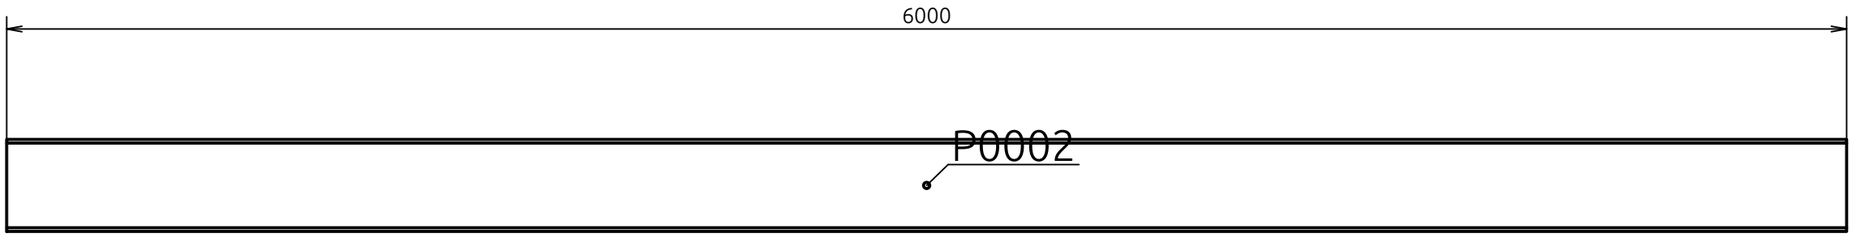

Вид спереди 1:20



Вид слева 1:20

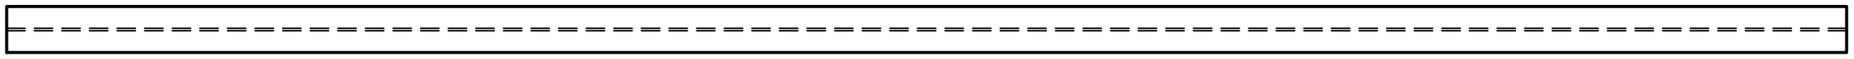

Вид сверху 1:20

Взам. инв. №

Подп. и дата

Инв. № подл.


Изм.	Кол.уч	Лист	№ док.	Подп.	Дата
Разраб.					
Пров.					
Н. контр.					

0000-КМД

Стадия	Лист	Листов
Р	1	3

Балка


Формат А3

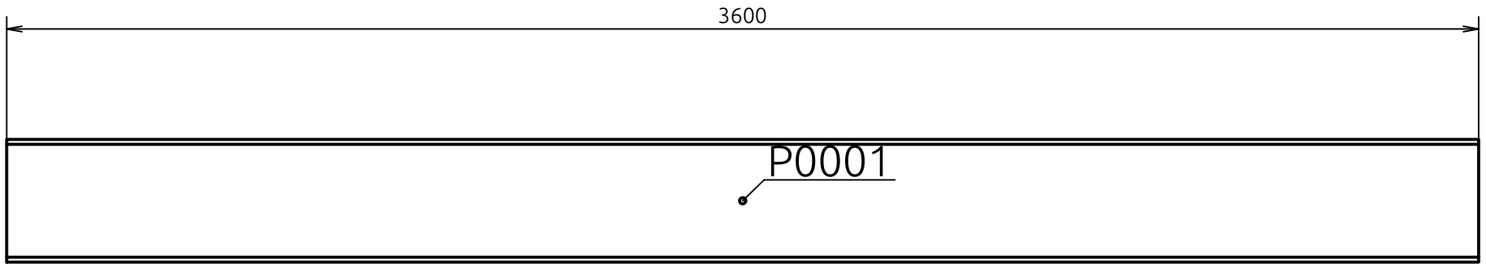

Вид спереди 1:15



Вид слева 1:15

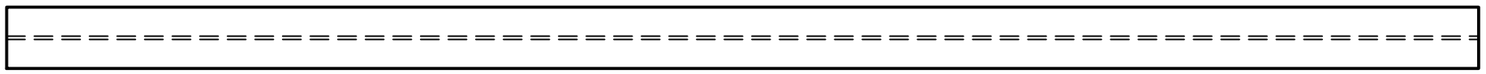

Вид сверху 1:15

Взам. инв. №

Подп. и дата

Инв. № подл.


Изм.	Кол.уч	Лист	№ док.	Подп.	Дата
Разраб.					
Пров.					
Н. контр.					

0000-КМД

Стадия	Лист	Листов
Р	2	

Колонна

Формат А3

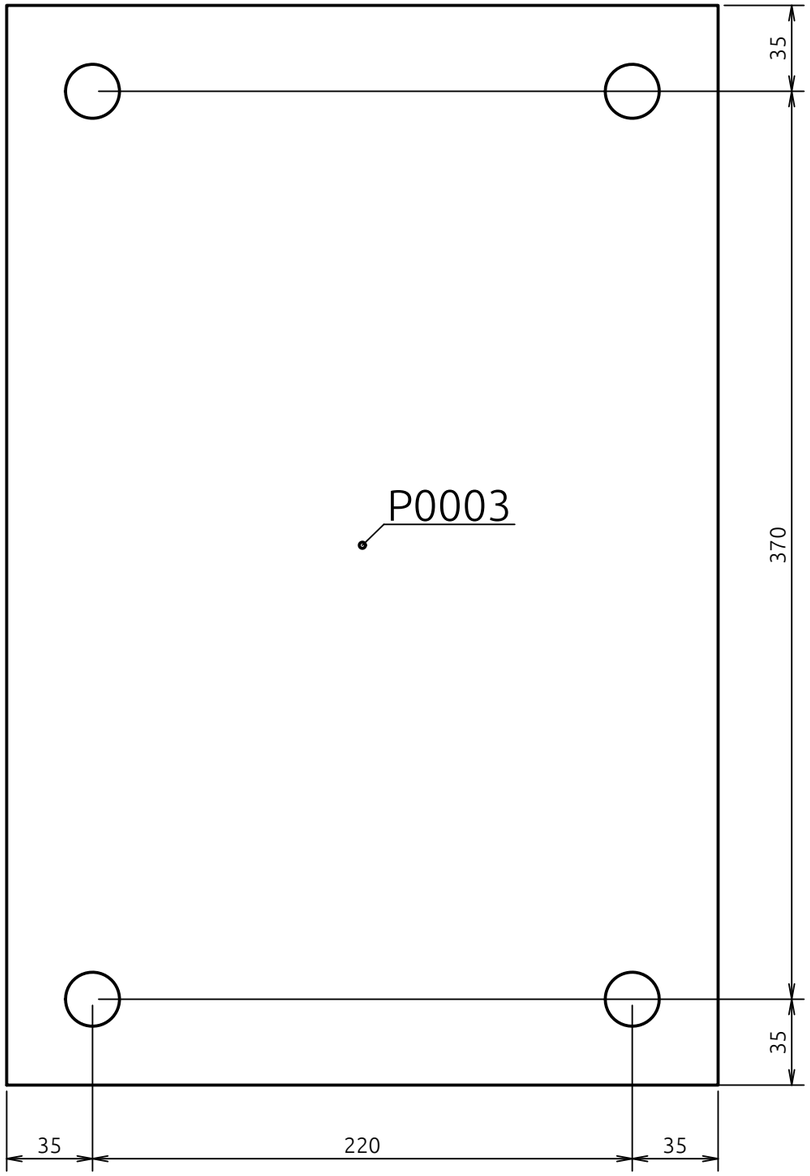

Вид на плиту 1:2,5

Взам. инв. №

Подп. и дата

Инв. № подл.

Изм.	Кол.уч	Лист	№ док.	Подп.	Дата
Разраб.					
Пров.					
Н. контр.					

0000-КМД

Стадия	Лист	Листов
Р	3	

Соединение — плита

Формат А3